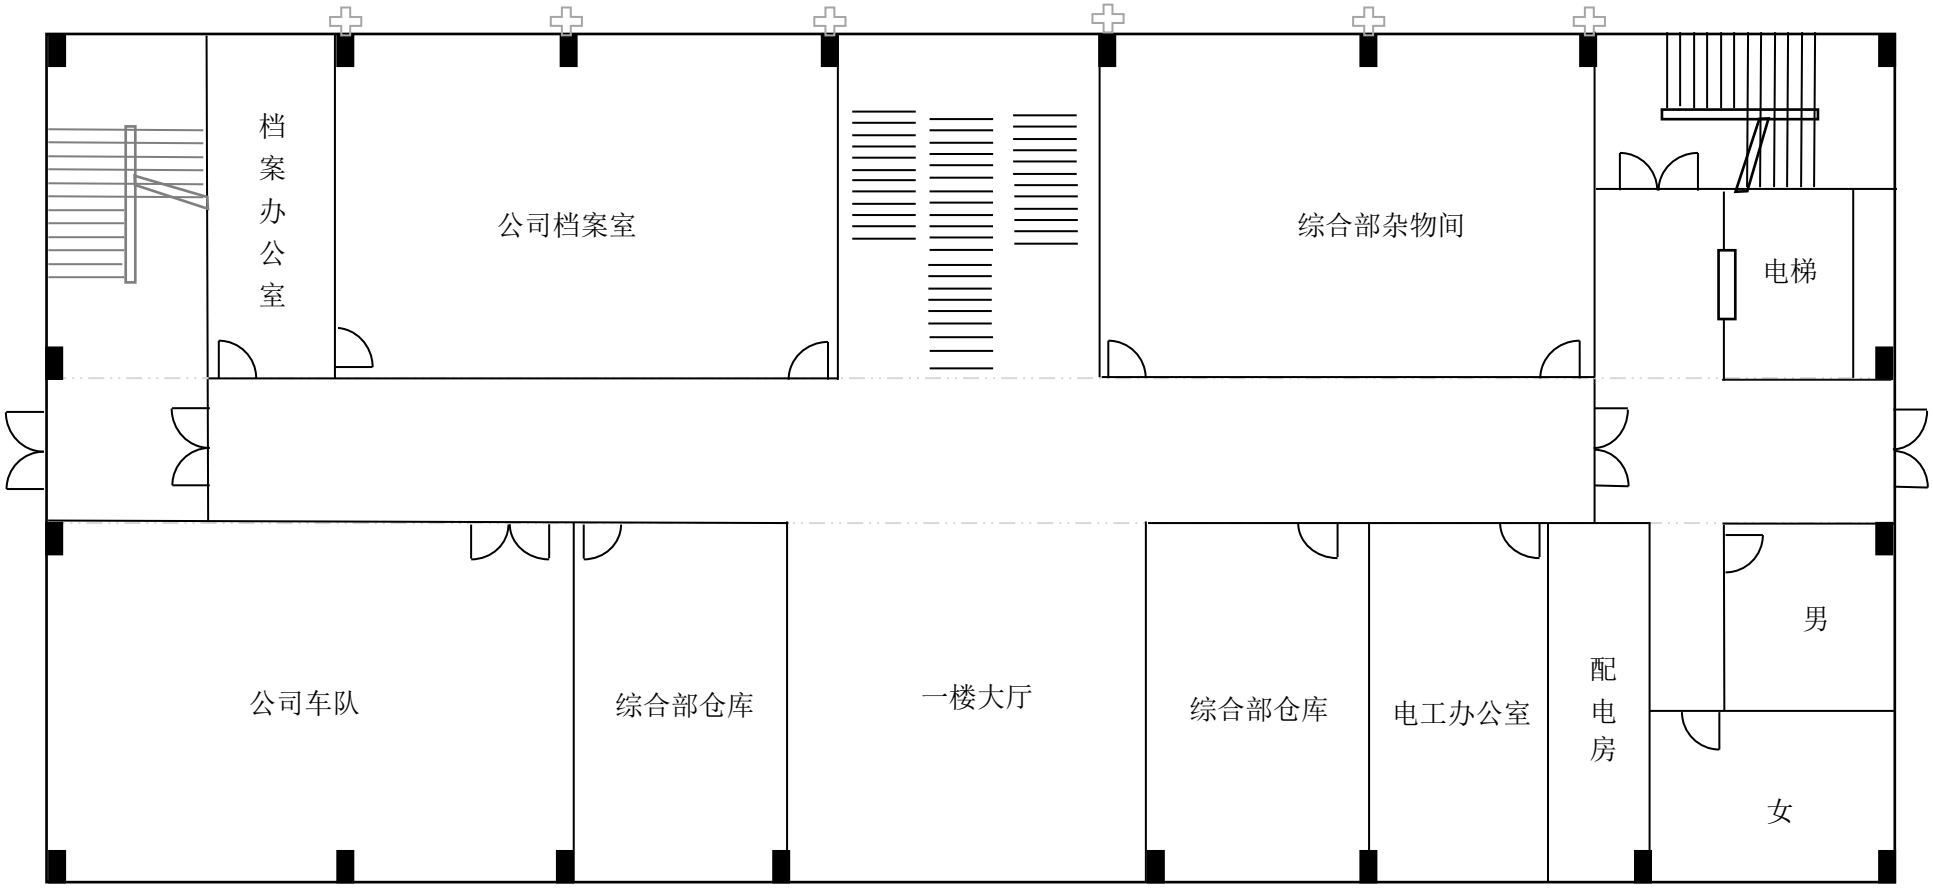

一楼

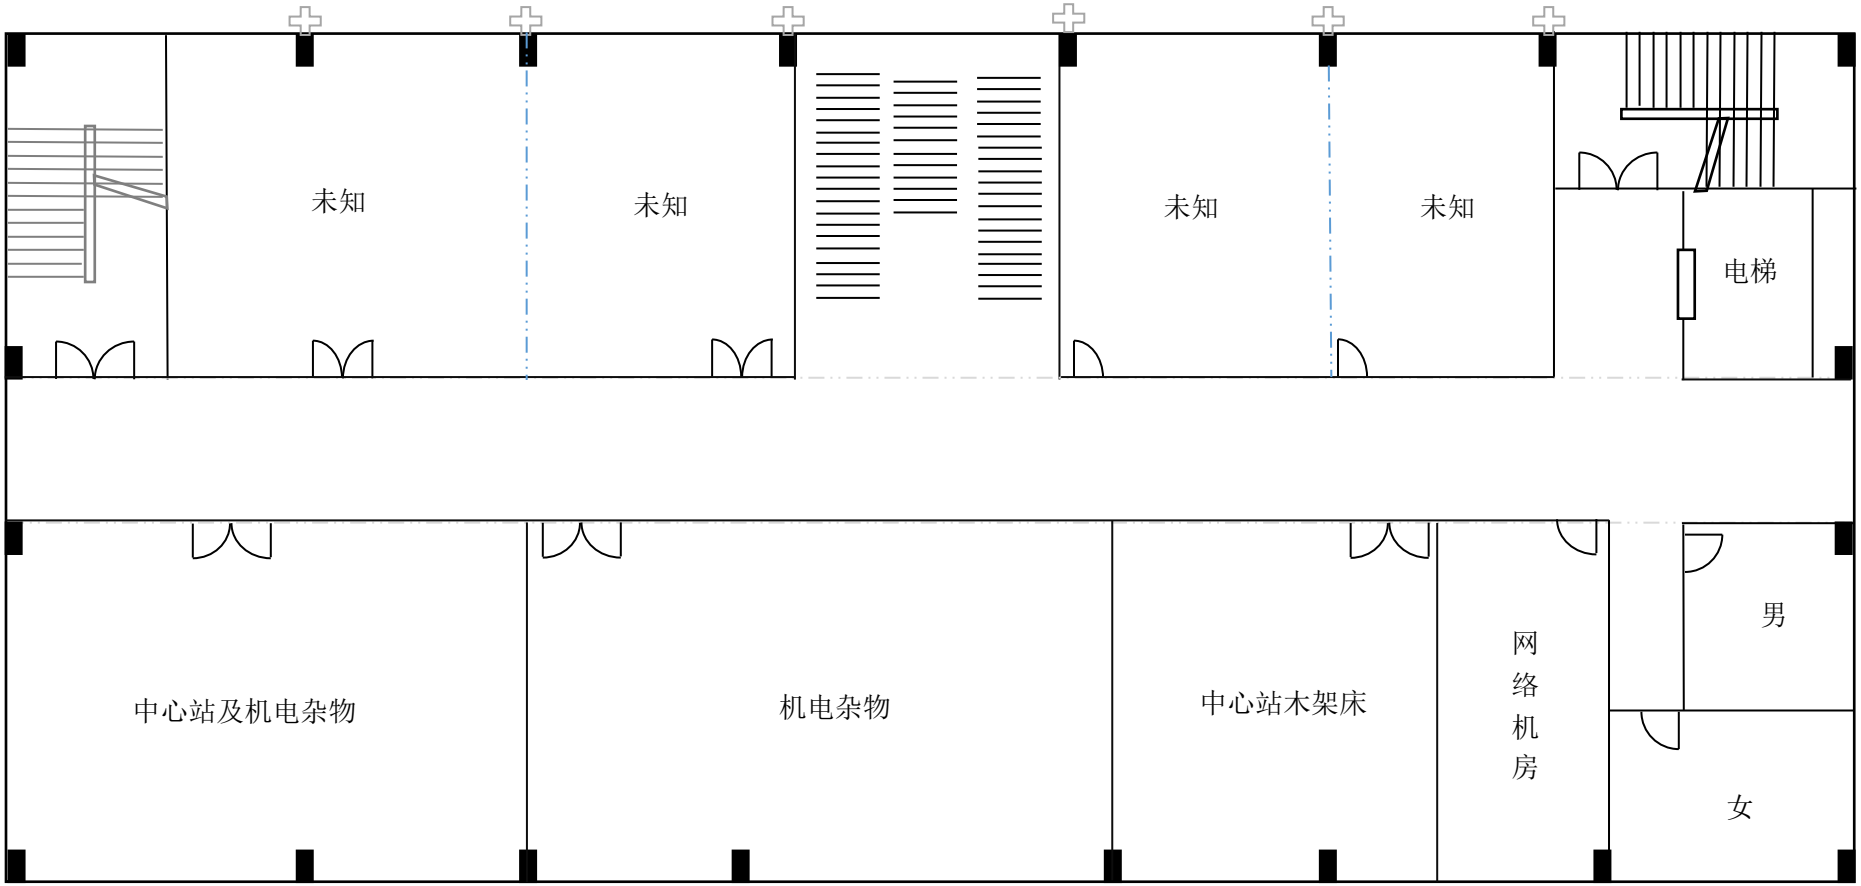

二楼